

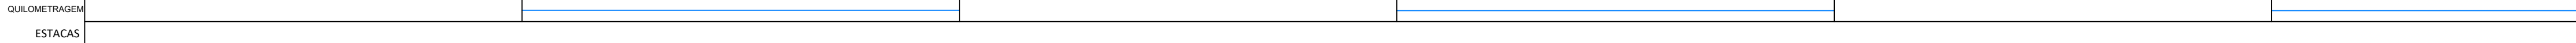


FLECHA MÁXIMA CONSIDERANDO AÇÃO DO VENTO A 60km/h =A 55°C , H = COM ALTURA MÍNIMA 3X70(70)

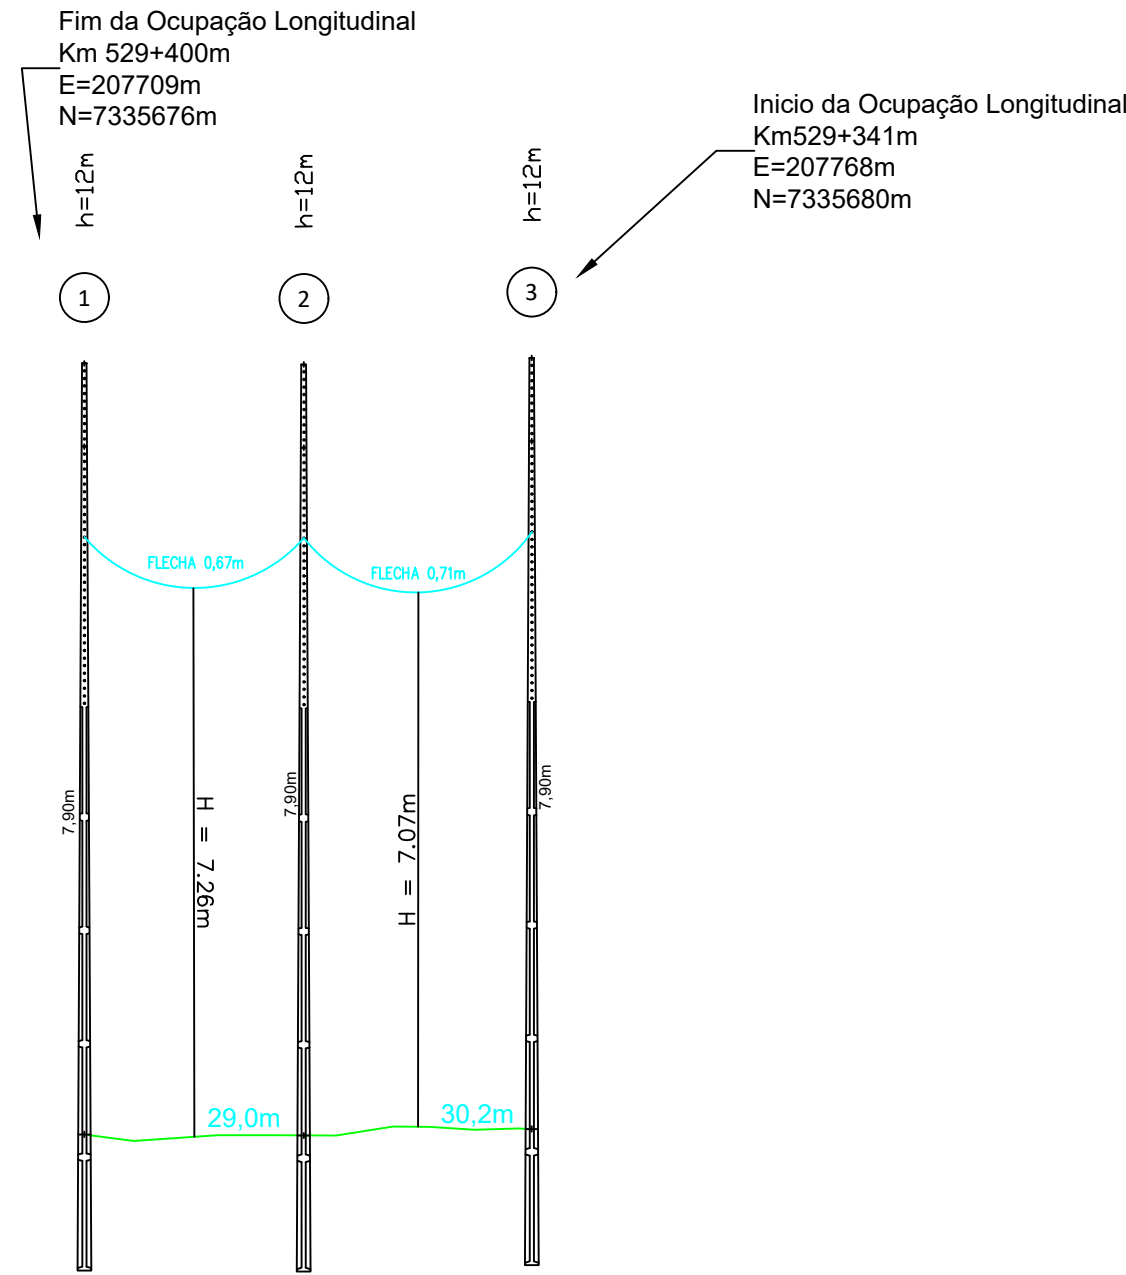

Perfil Longitudinal de Ocupação de Faixa de Domínio - Esc: 1:1000(long) / 1:100(h)

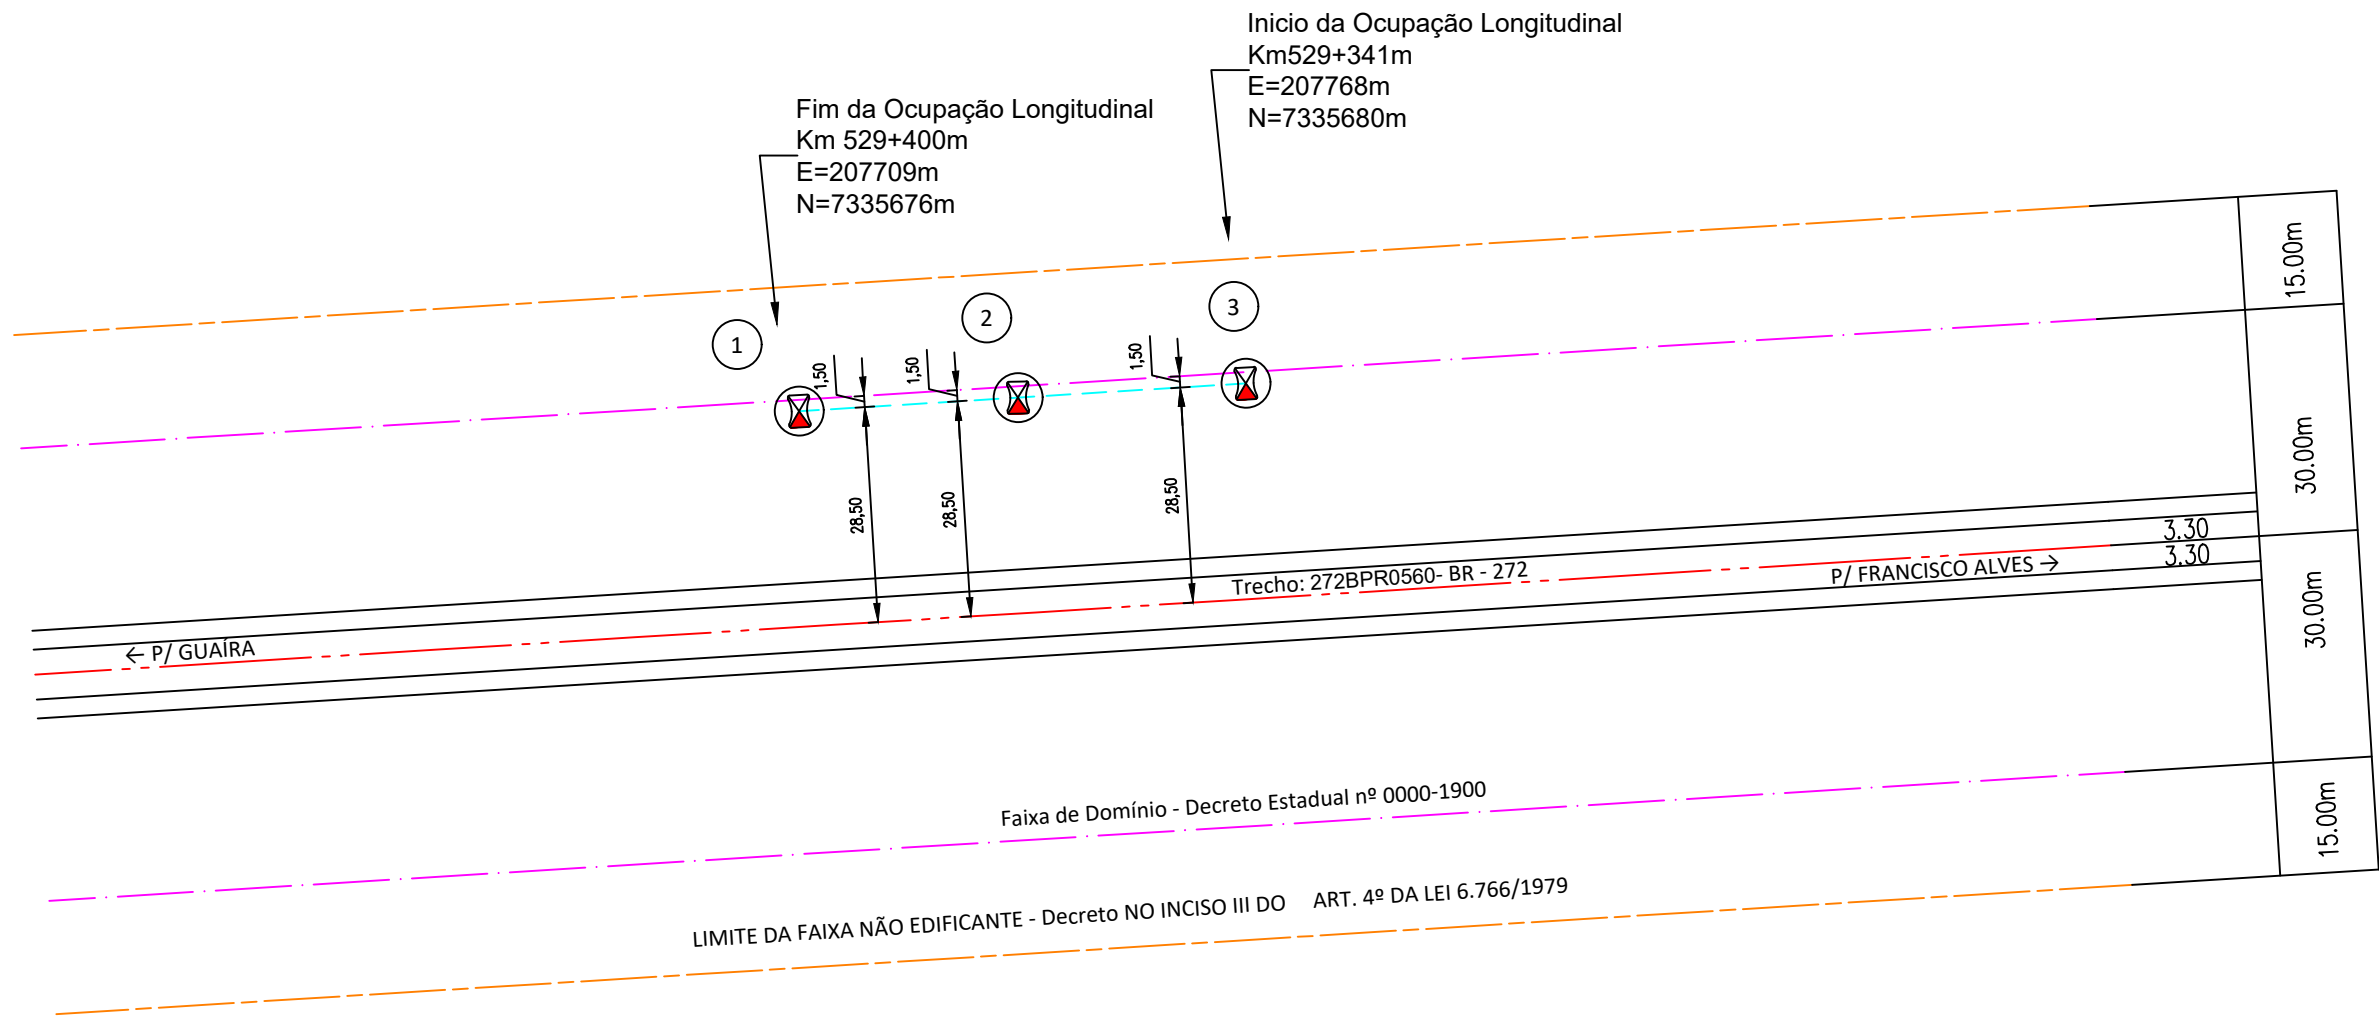

PLANIMÉTRICO 1:1000

CARACTERÍSTICAS ELÉTRICAS		CARACTERÍSTICAS MECÂNICAS DO CONDUTOR	
TENSÃO NOMINAL	220/127V	MATERIAL	Alumínio
NÚMERO DE FASES	3	CÓDIGO	20009716
CONDUTOR NEUTRO	70MM2	BITOLA	2/0 AWG
CONDUTOR CONTROLE	0	SEÇÃO TRANSVERSAL	70mm2
NÚMEROS DE CIRCUITOS	1	DIÂMETRO	10,2mm2
NÚMERO DE CONDUTORES POR FASE	1	MASSA LINEAR NOMINAL	928 kg/km
CORRENTE MÁXIMA ADMISSÍVEL P/ 27°C AMBIENTE E VENTO 2,2km/h	215A	MÓDULO DE ELASTICIDADE (FINAL)	7.000daN/mm ²
FREQUÊNCIA	60 Hz	CARGA DE RUPTURA	2020 daN
FLECHA MÁXIMA	0,770m	CARGA MÁXIMA DE TRABALHO (3%)	60,6 daN
		COEFICIENTE DE SEGURANÇA (* *)	2,13


1- (*) (*) RELAÇÃO ENTRE A CARGA DE RUPTURA PELA CARGA MÁXIMA DE TRABALHO;
A CAPACIDADE DE CONDUÇÃO DE CORRENTE E PARA TEMPERATURA NO CONDUTOR DE 50º C E AMBIENTE DE 40º C
VENTO DE 2,2km/h E COM SOL (RADIAÇÃO DE 1000W/m²)

- POSTE DE CONCRETO DUPLO T PROJETADO H = 12,0m

- POSTE DE CONCRETO DUPLO T EXISTENTE H = 13,5m

- POSTE DE CONCRETO DUPLO T EXISTENTE H = 12,0m

- REDE DE BAIXA TENSÃO PROJETADA

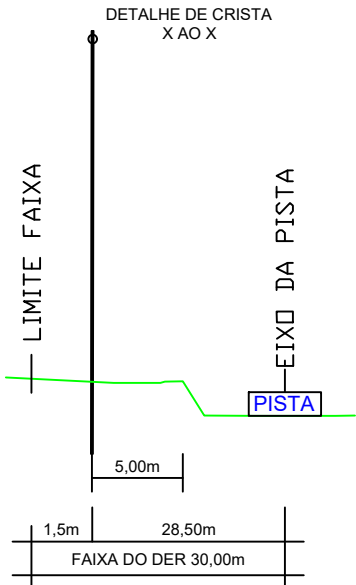

BR 272 - FRANCISCO ALVES

LOCAL: RODOVIA BR - 272 - OCUPAÇÃO LONGITUDINAL

LEVANTAMENTO : JACINTO

CALCULO : JACINTO

DESENHO : MARIA

CONF. : JACINTO

TRECHO: 272BPR0560 - ACESSO FRANCISCO ALVES

- ENTR: PR-496 (P/TERRA ROXA)

km Inicial 526+800m - km Final 553+800m

OCUPAÇÃO LONGITUDINAL km Inicial 529+341m - km Final 529+400m

CABO: INDICADO

ESCALAS - INDICADAS

FOLHA: 1/2

CONTRATO : AES Nº

PROJETO Nº 1721887

RESPONSÁVEL TÉCNICO:


JOÃO VICTOR PERGO ANACLETO

ENG. ELETRICISTA CREA PR- 234344/D

A1 = 841X594m



PLANTA DE SITUAÇÃO
SEM ESCALA

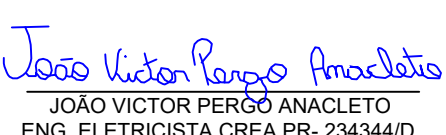RESPONSÁVEL TÉCNICO:  JOÃO VÍCTOR PERGO ANACLETO ENG. ELETRICISTA CREA PR- 234344/D		
TIPO DE OCUPAÇÃO	TRECHO	COMPRIMENTO
LONGITUDINAL	km 529+341 ao km 529+400m	59,00m
TOTAL		59,00m
 BR 272 - FRANCISCO ALVES		
LOCAL: RODOVIA BR - 272 - OCUPAÇÃO LONGITUDINAL		
TIPO DE OCUPAÇÃO PROET eletricidade telecomunicações	LEVANTAMENTO : JACINTO	TRECHO: 272BPR0560 - ACESSO FRANCISCO ALVES
	CALCULO : JACINTO	- ENTR: PR-496 (P/TERRA ROXA)
	DESENHO : MARIA	km Inicial 526+800m - km Final 553+800m
	CONF. : JACINTO	OCUPAÇÃO LONGITUDINAL km Inicial 529+341m - km Final 529+400m
CABO: INDICADO	ESCALAS - INDICADAS	FOLHA: 2/2 CONTRATO : AES Nº PROJETO Nº 1721887

SINALIZAÇÃO DE OBRAS Rodoviárias - SINALIZAÇÃO TEMPORÁRIA

RODOVIA PR - 340 - OCUPAÇÃO LONGITUDINAL DE REDE DE ENERGIA ELÉTRICA 34,5KV, NO LIMITE DA FAIXA DE DOMÍNIO

BLOQUEIO ESTIMADO DA PISTA DE 5 MINUTOS

