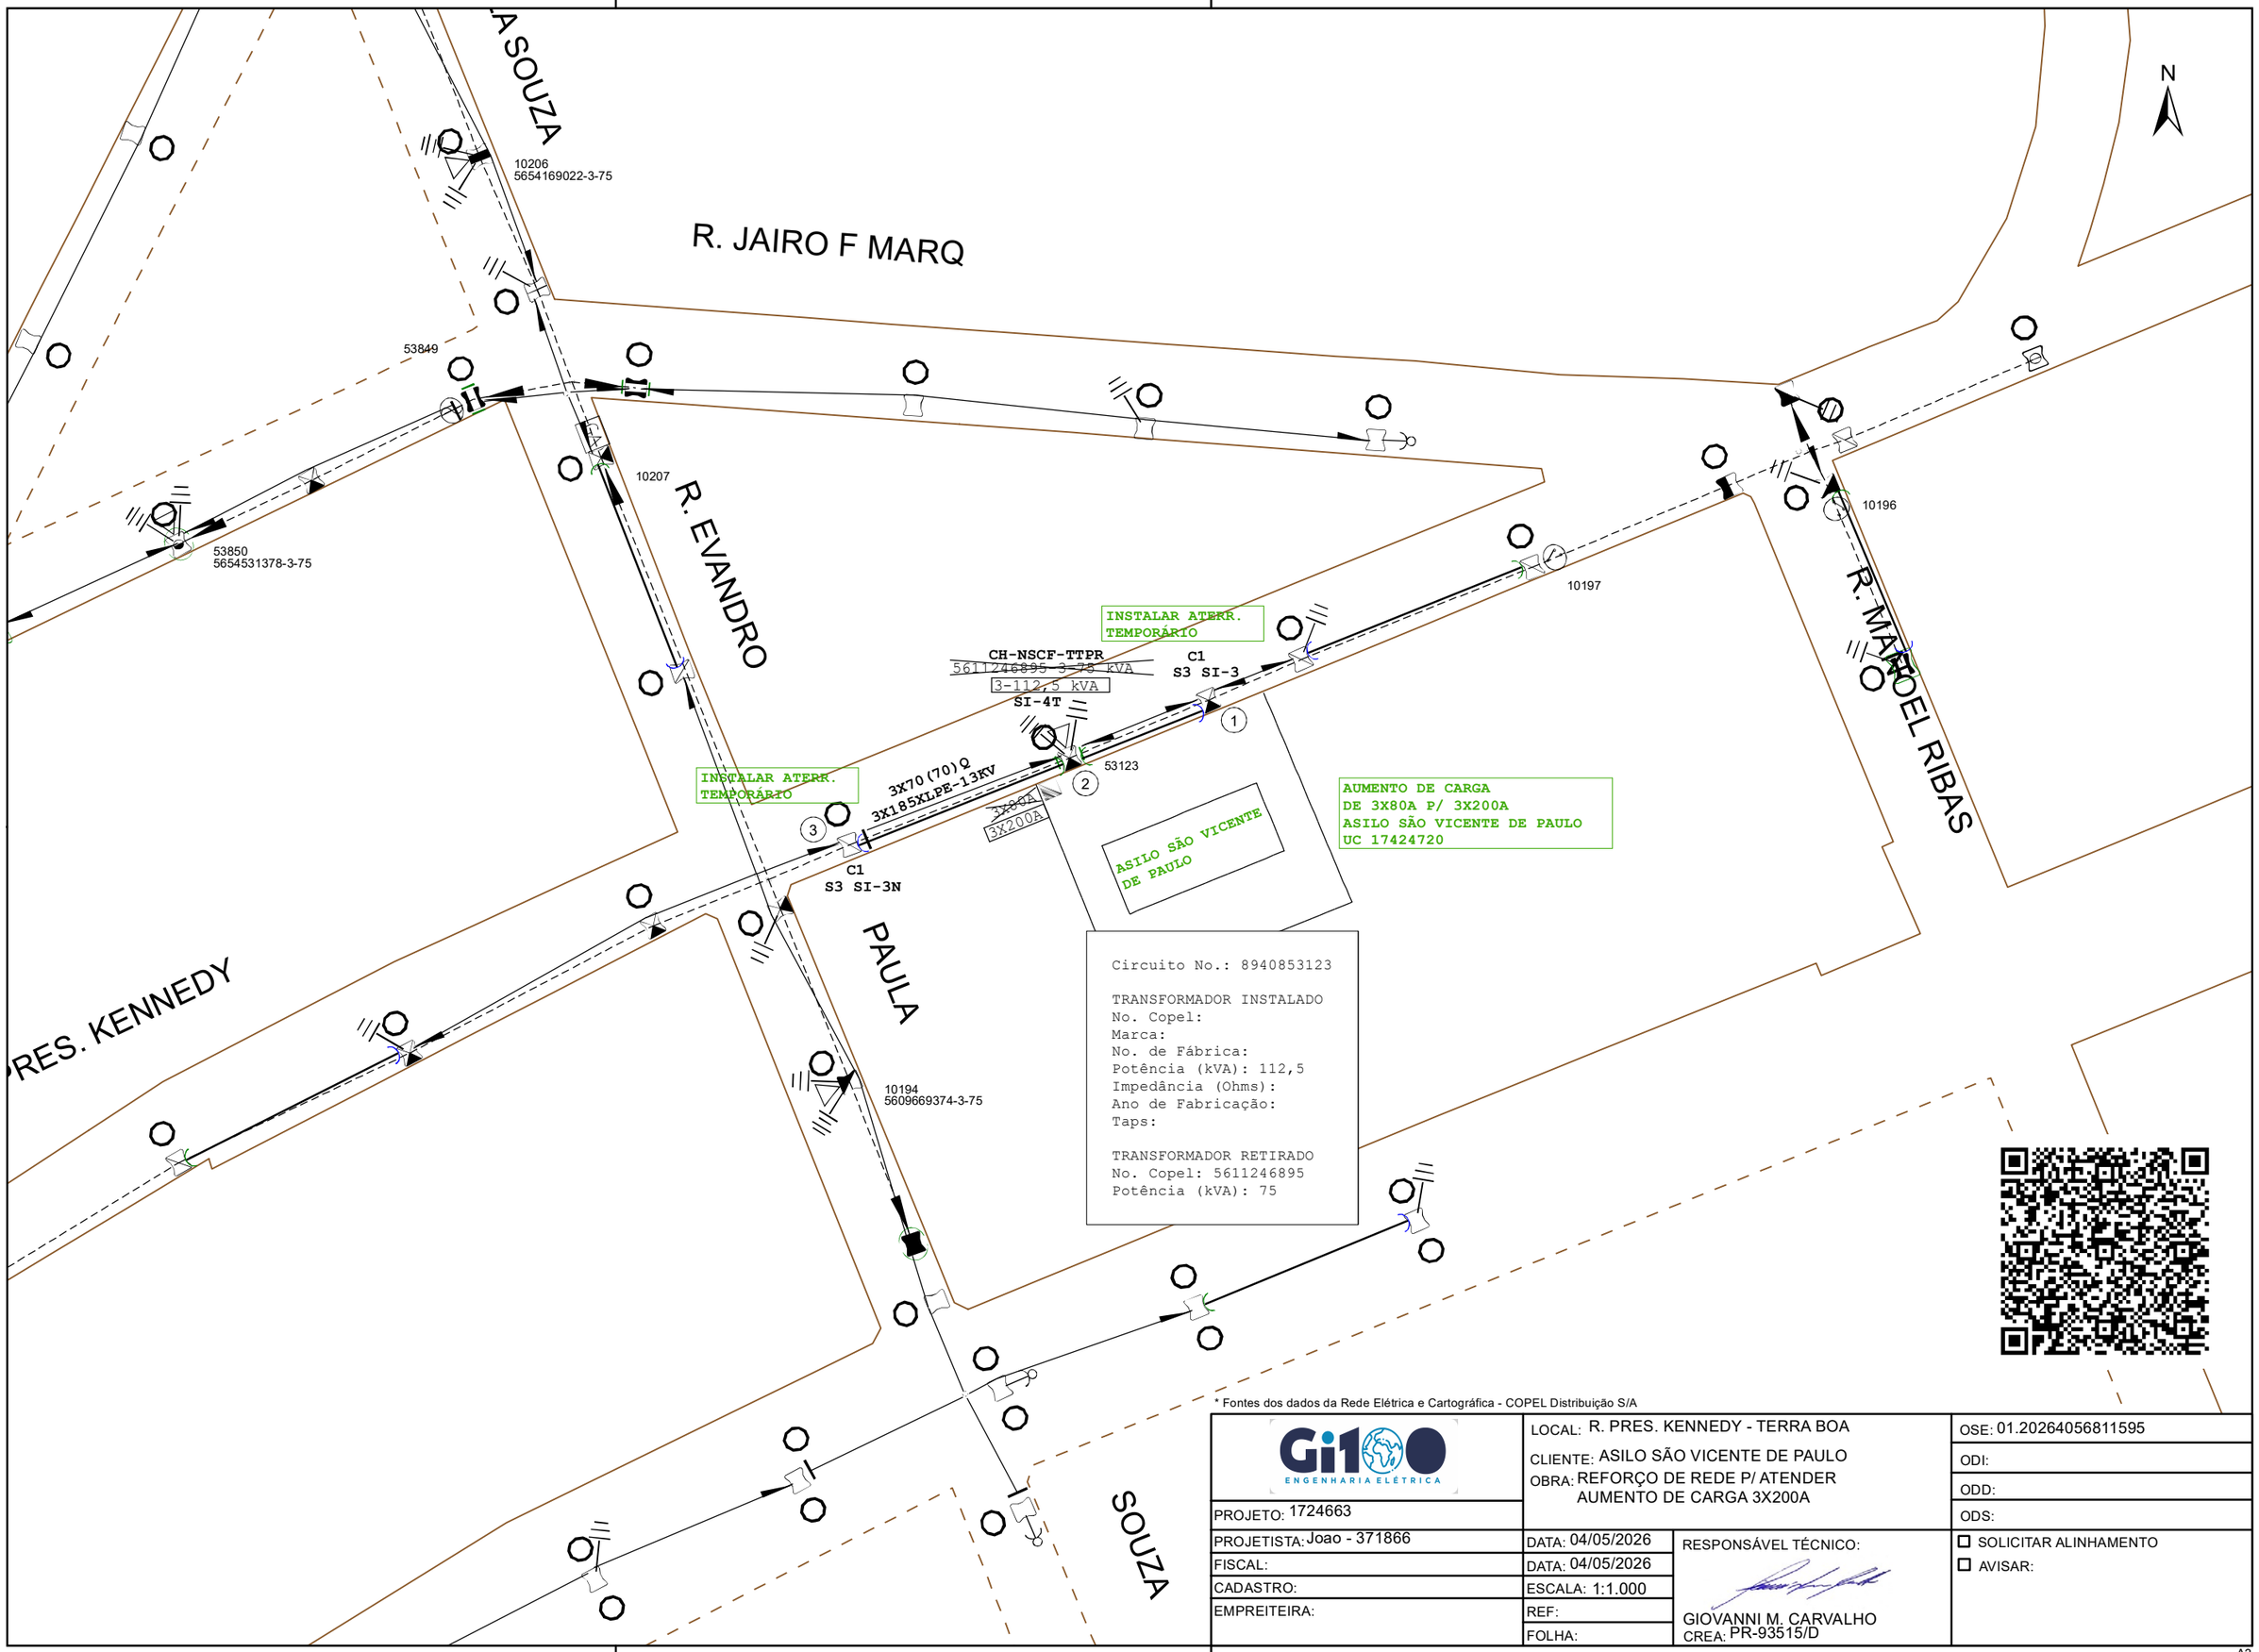

* Fontes dos dados da Rede Elétrica e Cartográfica - COPEL Distribuição S/A

Gi100 ENGENHARIA ELÉTRICA	LOCAL: R. PRES. KENNEDY - TERRA BOA CLIENTE: ASILO SÃO VICENTE DE PAULO OBRA: REFORÇO DE REDE P/ ATENDER AUMENTO DE CARGA 3X200A		OSE: 01.20264056811595 ODI: ODD: ODS:
PROJETO: 1724663			
PROJETISTA: Joao - 371866	DATA: 04/05/2026	RESPONSÁVEL TÉCNICO:	☐ SOLICITAR ALINHAMENTO
FISCAL:	DATA: 04/05/2026		☐ AVISAR:
CADASTRO:	ESCALA: 1:1.000		
EMPREITEIRA:	REF:	GIOVANNI M. CARVALHO CREA: PR-93515/D	
	FOLHA:		

A3